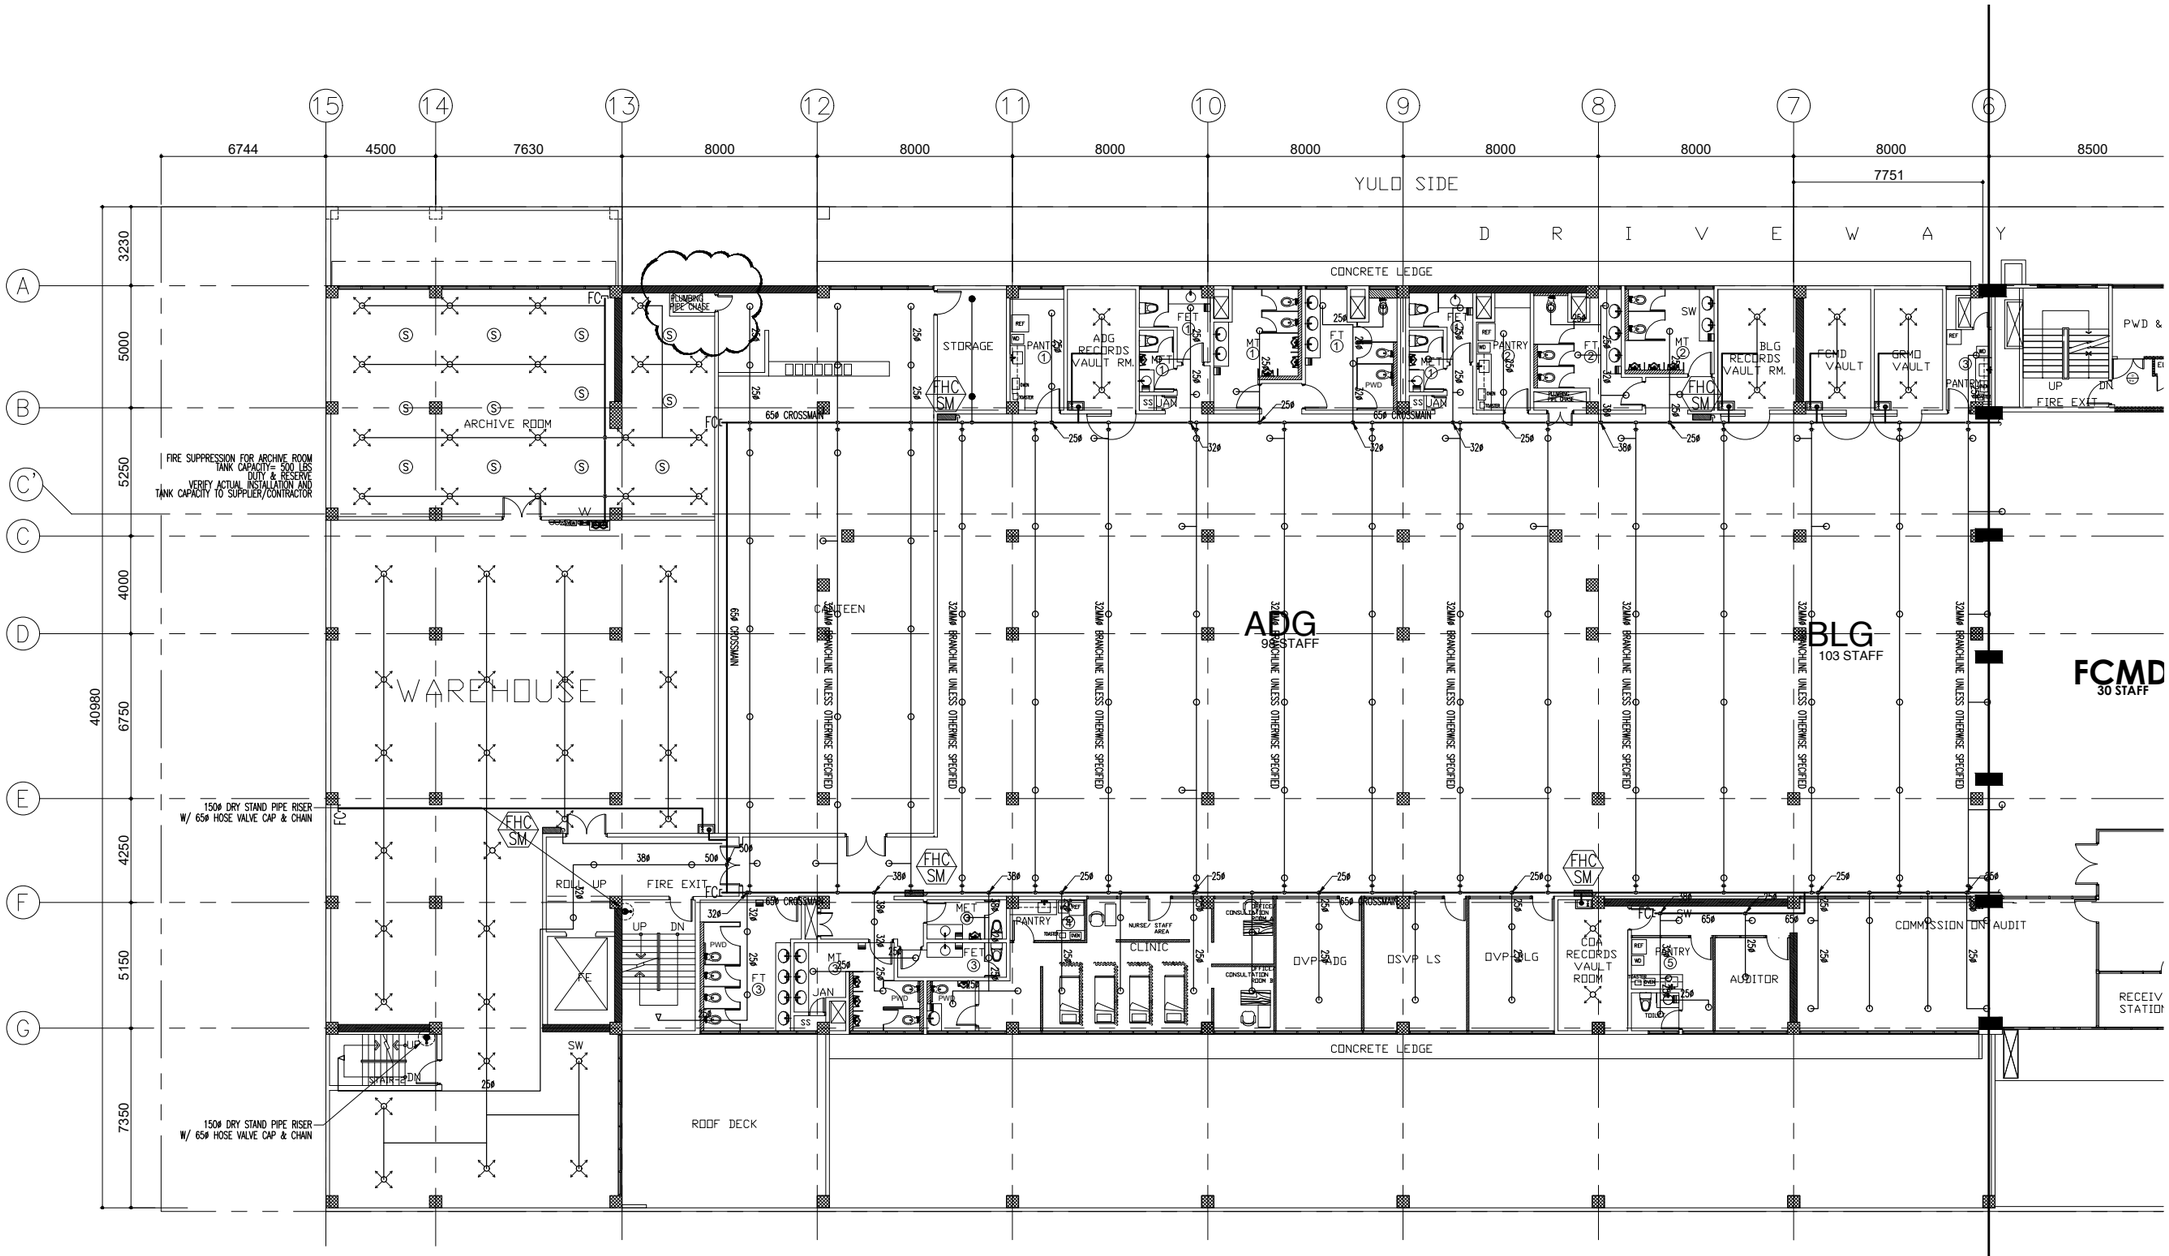

NOTE: FIRE SUPPRESSION FOR EE ROOMS, GENSETS, VAULTS AND WAREHOUSE WILL BE PROVIDED BY CLIENT.
NOTE: FIRE SUPPRESSION FOR INSTALLATION AND CAPACITY ARCHIVE ROOM SHALL BE VERIFIED TO SUPPLIER & CONTRACTOR.

THIRD FLOOR PLAN
FIRE PROTECTION LAYOUT

A FP-04 SCALE 1:100

GRAPHIC SCALE: 0 2 4 6 8
SCALE 1:100 M
NOTE: CHECK GRAPHIC SCALE PRIOR TO SCALING

CONSULTANT		OWNER	APPROVED BY:	PROJECT TITLE	SHEET CONTENT/S :	ISSUE NO.	REVISIONS	NO.	DATE		DATE	SHEET NO.
E. H. SISON ENGINEERS, CO. ENGINEERS * PLANNERS * CONSULTANTS 3431 GUERNICA ST., PALANAN, MAKATI CITY TEL. Nos. 8317115, 8337030	RAMON D. AGUILOS PROFESSIONAL MECHANICAL ENGINEER PTR NO.: 2464195 D — PRC NO.: 2736 DATE: 01-05-22 — TIN. NO.: 137-133-799 PLACE: QUEZON CITY	PDIC	CYRUS T. GALANG VICE PRESIDENT ADMINISTRATIVE SERVICES GROUP	RENOVATION OF PDIC BUILDING IN CHINO ROCES LOCATION: 2228 CHINO ROCES AVENUE, MAKATI CITY	THIRD FLOOR PLAN FIRE PROTECTION LAYOUT					DESIGNED BY: RDAEC CADD BY: RJA CHECKED BY: APPROVED BY: SCALE: AS SHOWN		FP-04