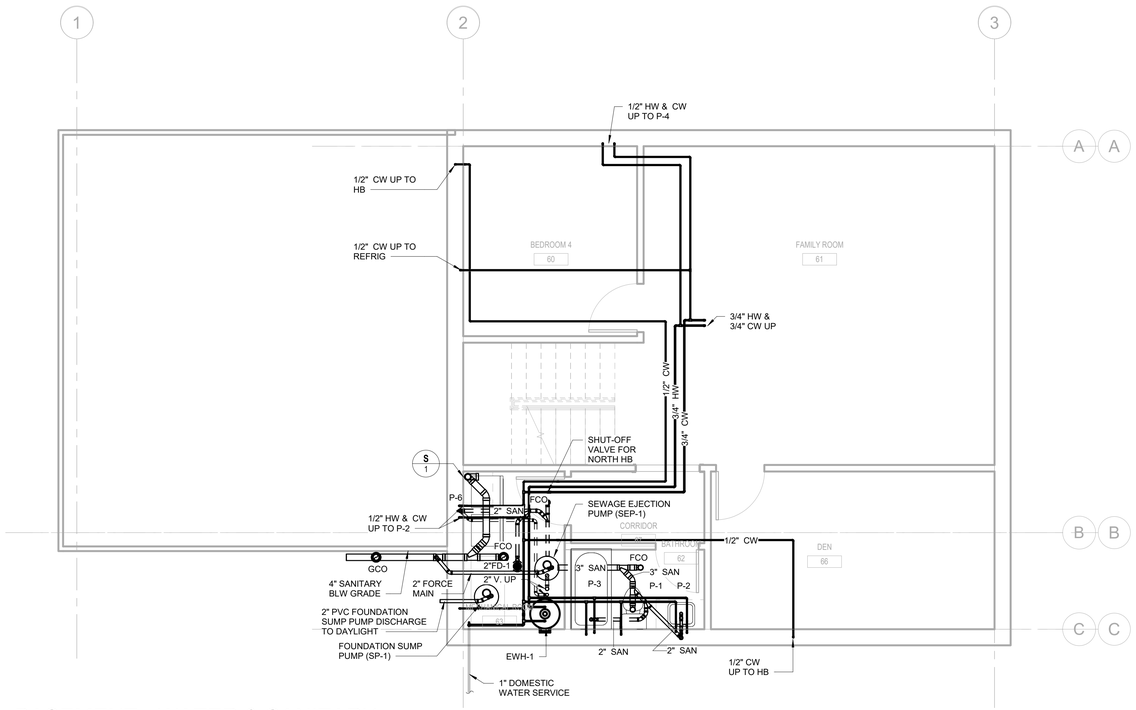

1 BASEMENT - WATER & SANITARY
1/4" = 1'-0"

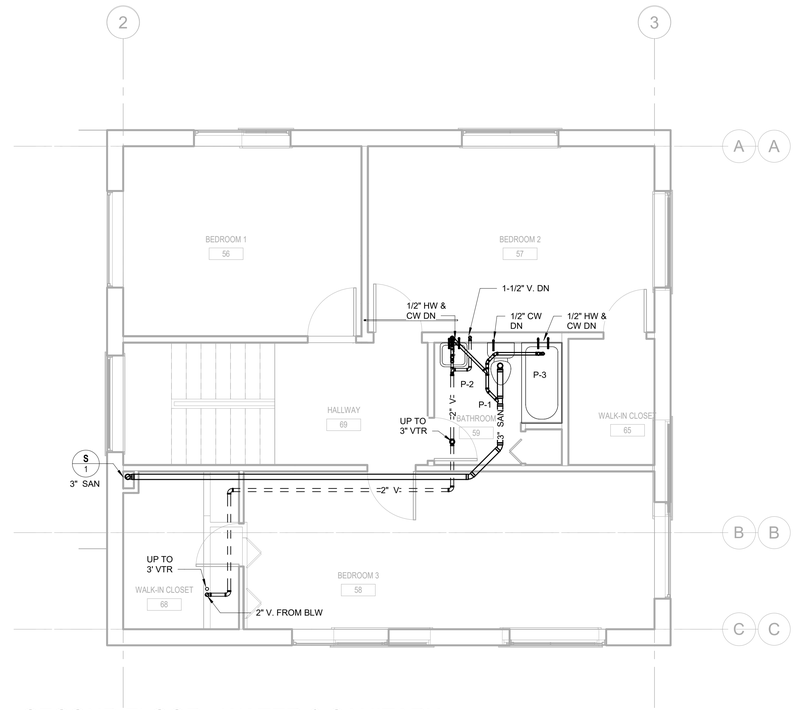

3 SECOND FLOOR - WATER & SANITARY
1/4" = 1'-0"

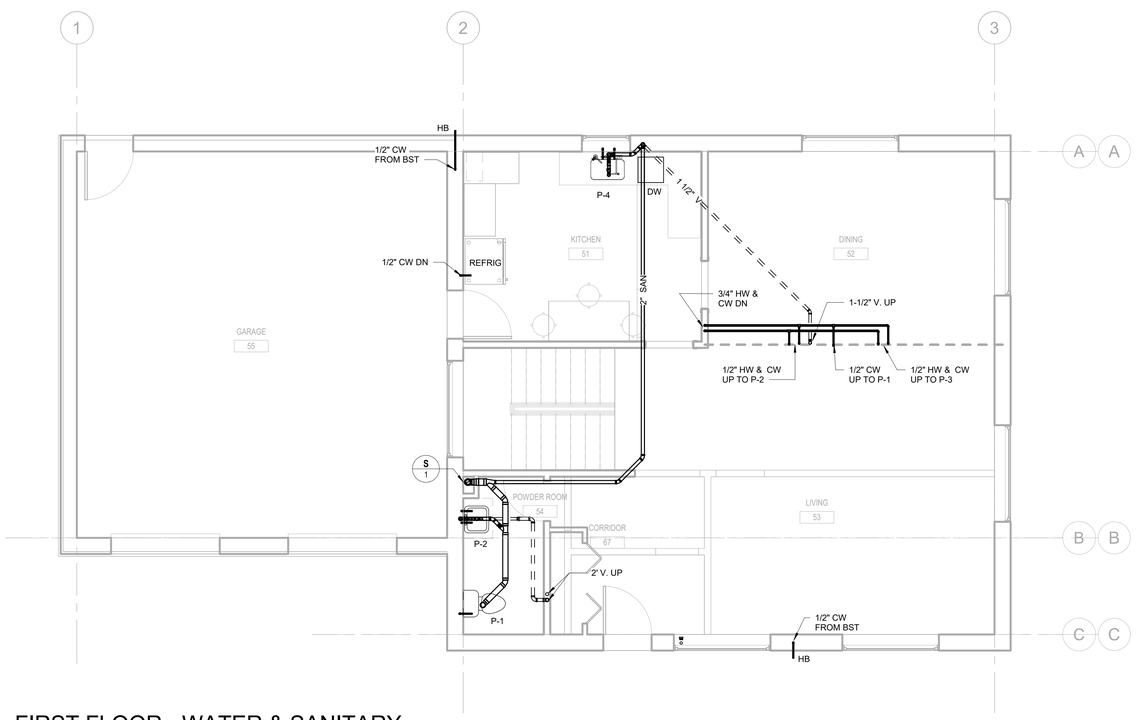

2 FIRST FLOOR - WATER & SANITARY
1/4" = 1'-0"

REVISION	DESCRIPTION	BY	DATE

ARCHITECT

MEP. ENG.

NIST

FOR OFFICIAL USE ONLY

U.S. DEPARTMENT OF COMMERCE

OFFICE OF FACILITIES & PROPERTY MANAGEMENT

NIST – SINGLE FAMILY DETACHED HOME MULTI STORY

PLUMBING FLOOR PLANS

P101

SH. NO. ___ OF ___ DWG. P101

APPROVED BY	DATE	SPONSOR	DATE	MAINTENANCE ENG. OFF.	DATE	ENVIRONMENTAL MANAGEMENT	DATE	SAFETY	DATE	SHED – NIST FIRE MARSHAL/AHJ	DATE	FACILITIES ENGR. OFF.	DATE	PROJECT LEADER	DATE	DRAWN BY	DATE	PROJECT/ W.O. #
														VAY		AA	08/15/2022	Project Number