CEILING SOFFIT FRAMING PLAN NOTES

1. FOR TYPICAL DETAILS SEE SHEET S5.02. FOR GENERAL NOTES SEE SHEET S1.10.
2. SEE ARCHITECTURAL DRAWINGS TO VERIFY LOCATION AND DIMENSIONS OF ALL SOFFITS.
3. FOR COLD FORMED STEEL DETAILS, SEE SHEET S5.03
4. UNISTRUT MEMBERS SUPPORTING CEILING SOFFITS ARE NOT SHOWN FOR CLARITY. SEE DETAILS 11 AND 12 ON SHEET S5.03

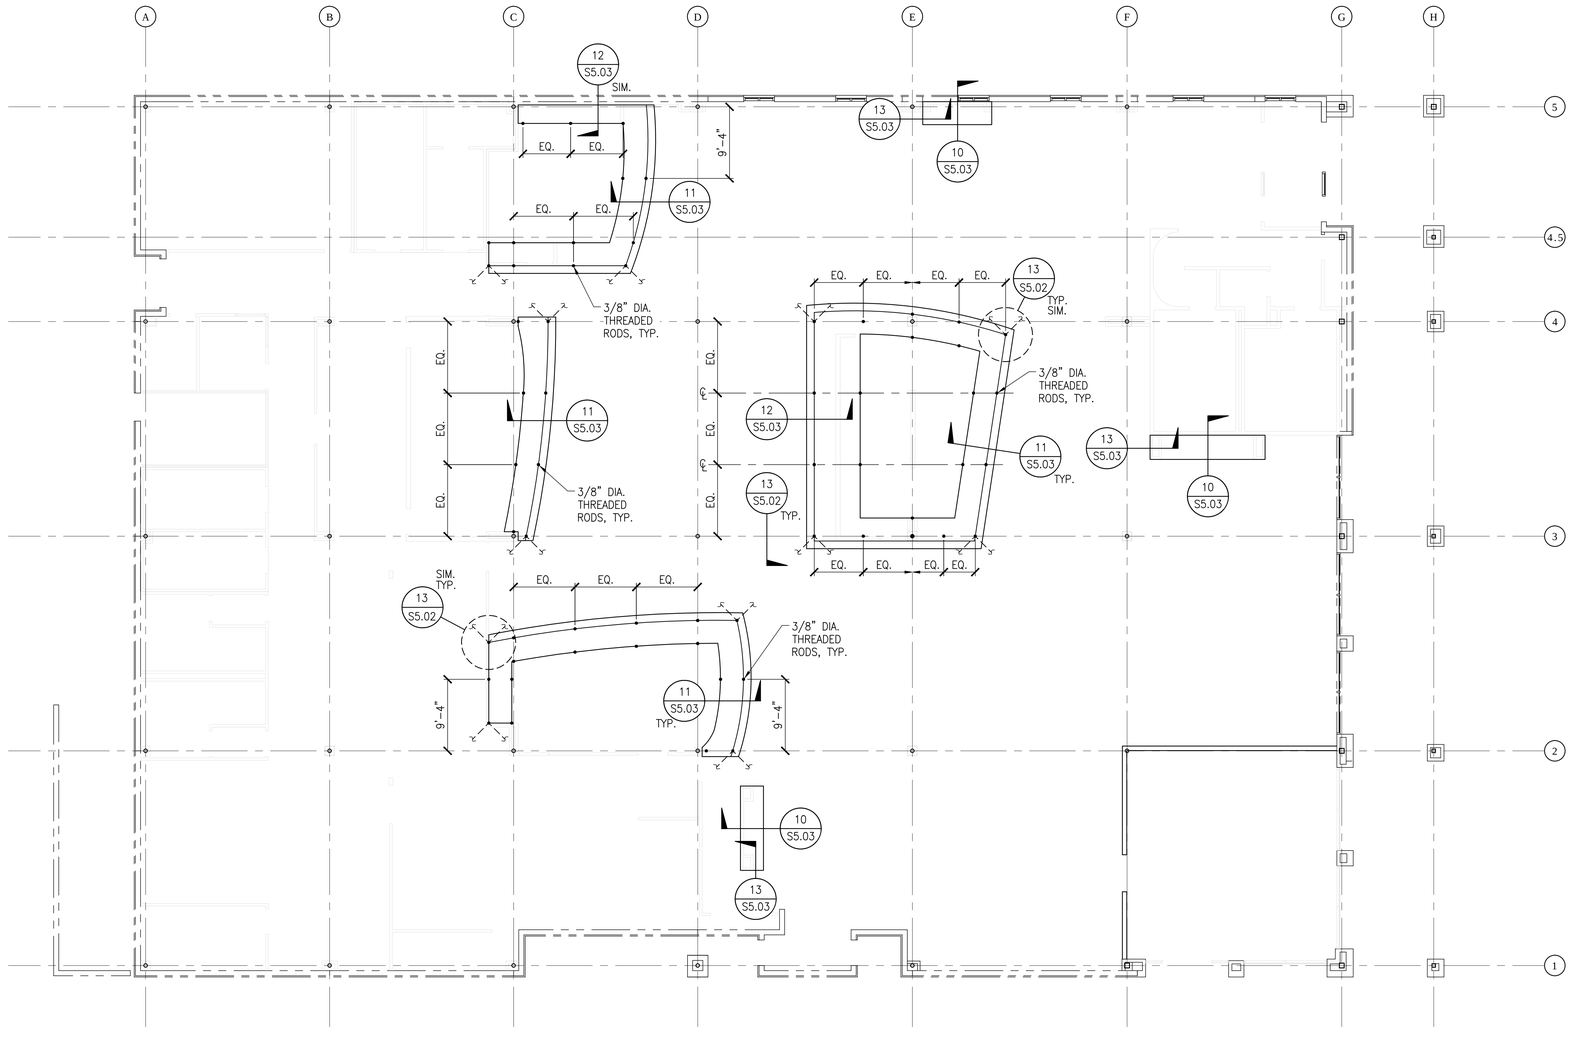

CEILING SOFFIT FRAMING PLAN
1/8" = 1'-0"

NORTH

DWL ARCHITECTS + PLANNERS, INC.
2333 N. Central Ave.
Phoenix, AZ 85004
tel 602.264.9731
dwlarchitects.com

THOMAD Engineering LLC
Structural Engineering Consulting
4535 W. RUSSELL ROAD
SUITE 12
LAS VEGAS, NV 89118
TEL (702) 388-7755
FAX (702) 388-7766
www.thomadengr.com

JOB #: 1111

UNIVERSITY OF NEVADA, LAS VEGAS
ARAMARK - STUDENT DINING COMMONS ALTERATION
4505 S. MARYLAND PARKWAY
LAS VEGAS, NV. 89119

ARAMARK
Innovative Dining Solutions
ARAMARK CORPORATION
ARAMARK INNOVATION CENTER
WANAMAKER BUILDING, 5th FLOOR
PHILADELPHIA, PA 19107

1 REVISIONS 06/06/11
2 PERMIT REVIEW 06/27/11
3 PERMIT REVIEW 07/08/11

CONSTRUCTION DOCUMENTS

© COPYRIGHT 2011
DWL ARCHITECTS + PLANNERS, INC.

KEY:

SHEET TITLE:
CEILING SOFFIT FRAMING PLAN

SHEET NUMBER:
S2.21

DRAWN BY:	REVIEWED BY:
EK	SN/MT
DATE: 06/27/11	PROJECT NUMBER: 1101.00