PRODUCED BY AN [redacted]

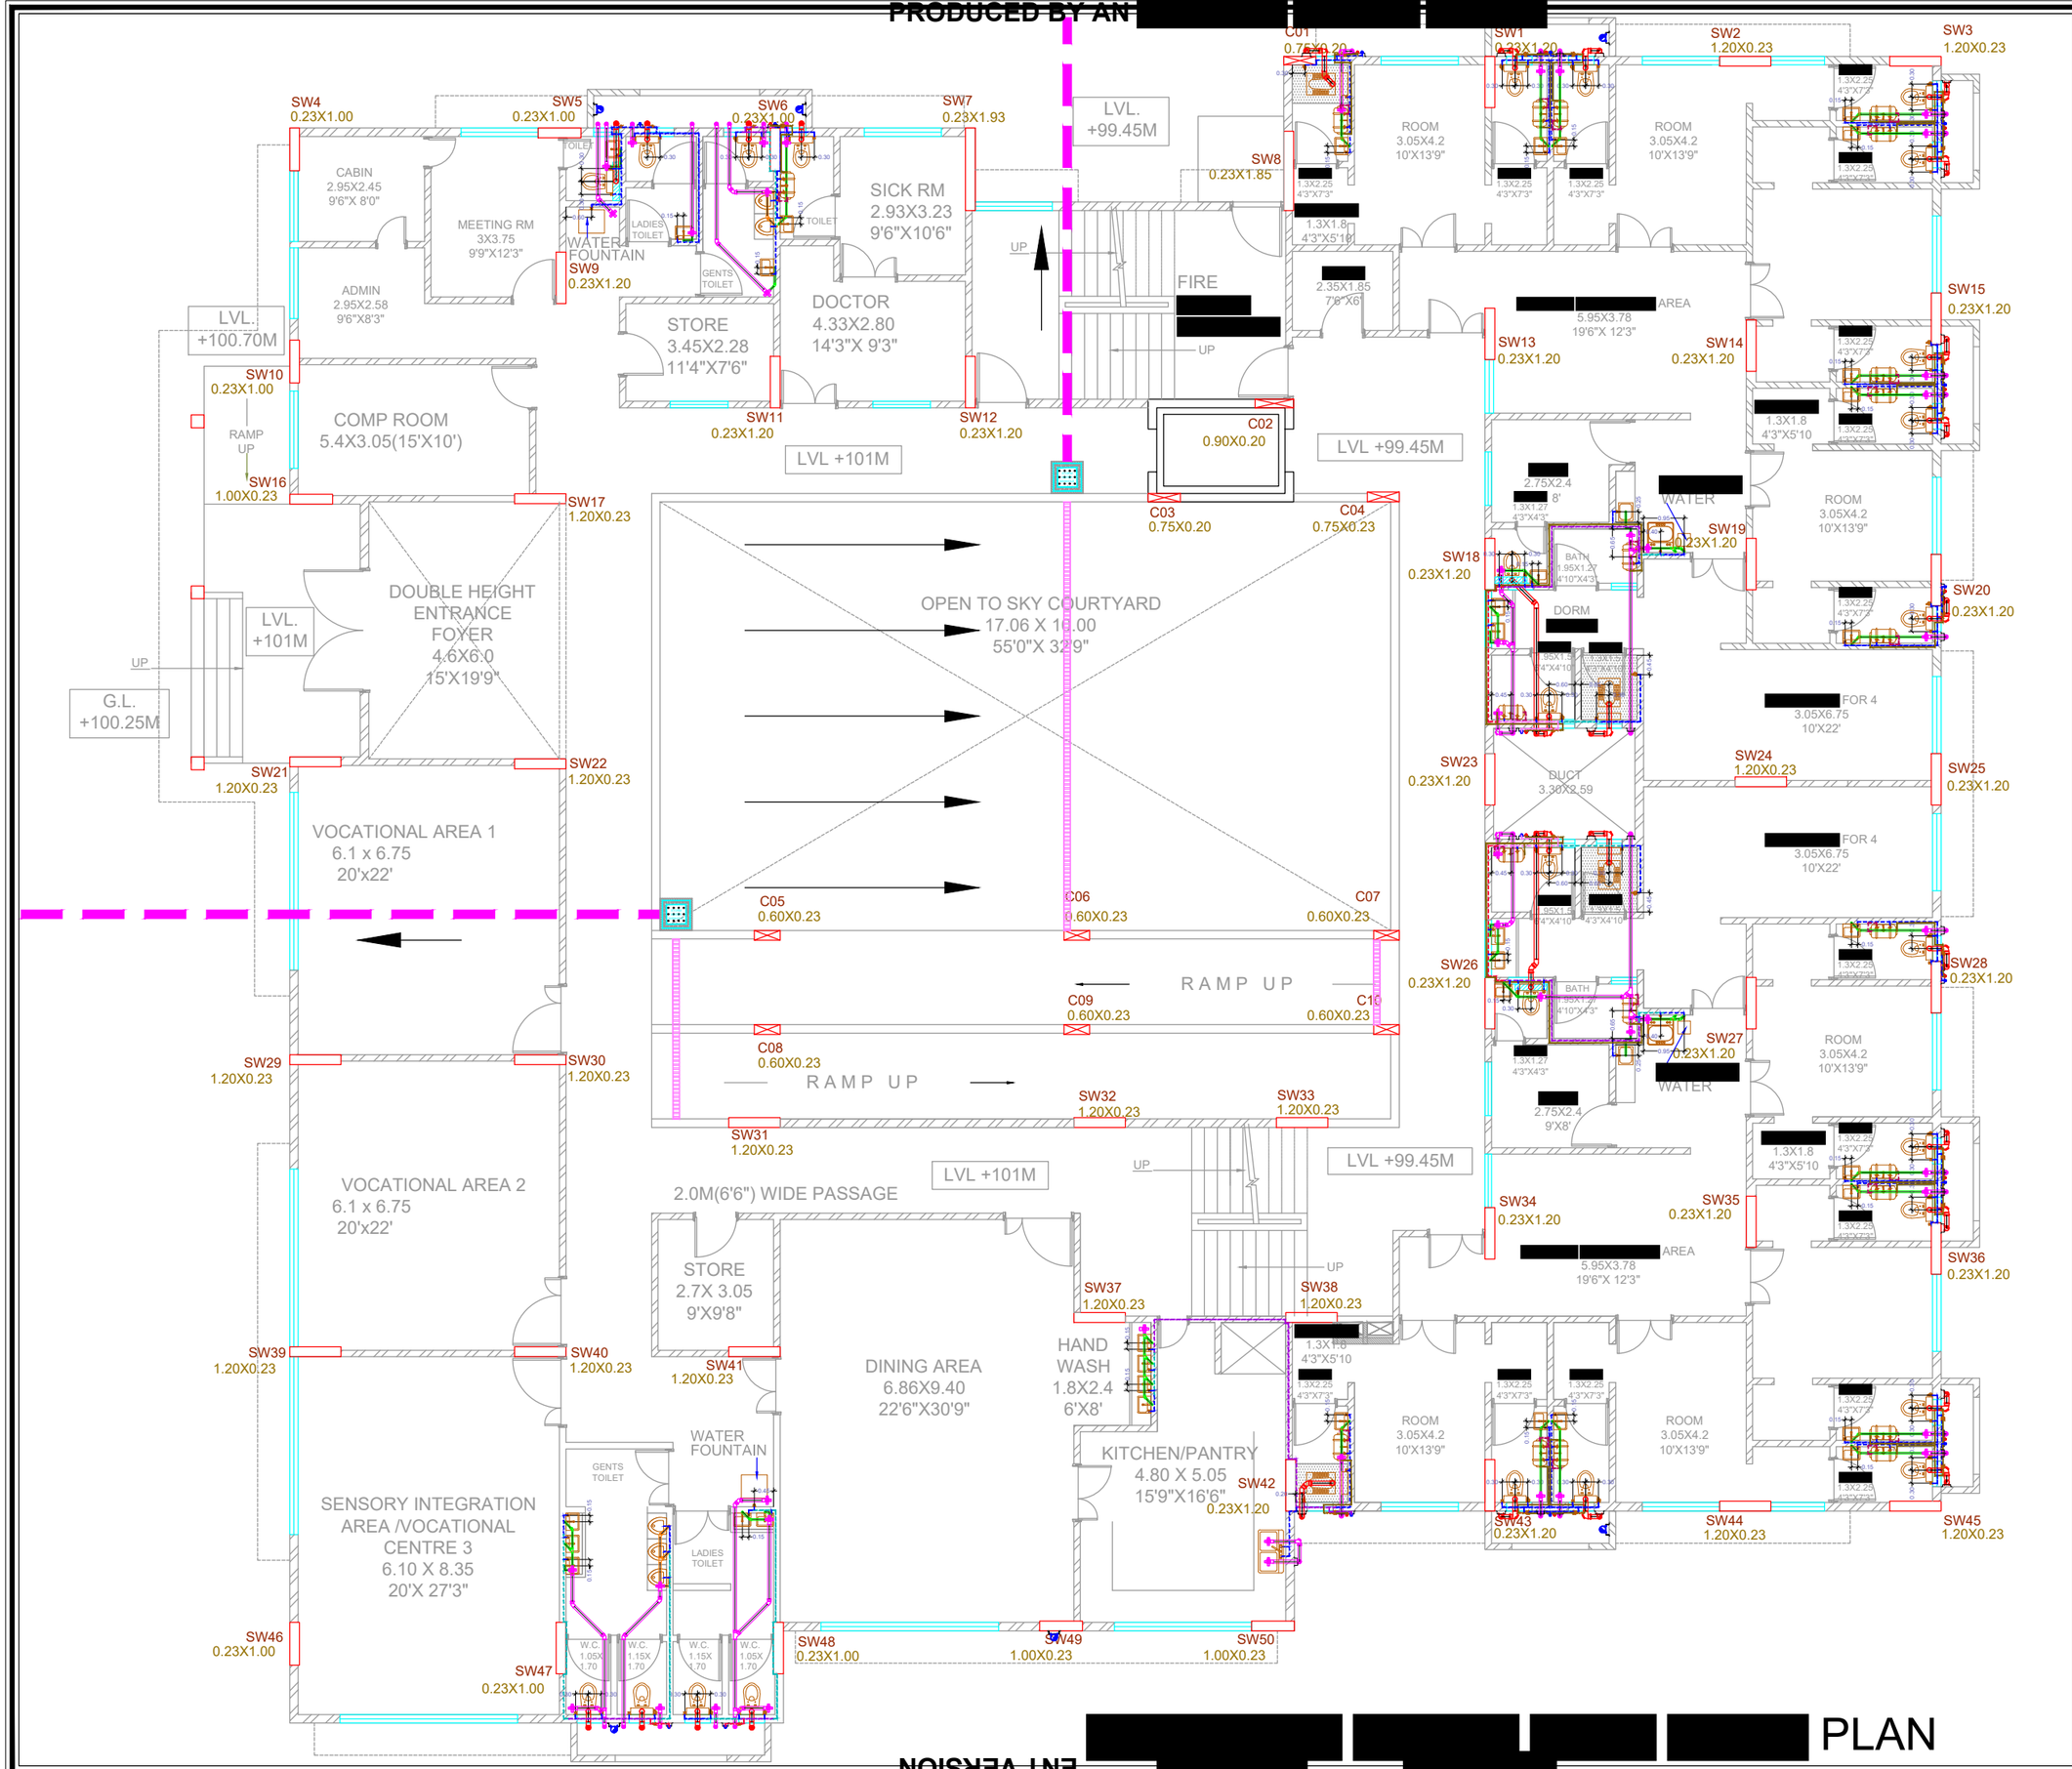

[redacted] PLAN

[redacted]	M/167/04
	R5
	02/03
[redacted]	[redacted] tants Pvt. Ltd. [redacted] COPY [redacted] June-30
[redacted]	
[redacted]	[redacted] PIPE [redacted] TYPE) Ø 110 mm
[redacted]	[redacted] PIPE [redacted] 'B' TYPE) Ø 75 mm
[redacted]	[redacted] PIPE [redacted] 'B' TYPE) Ø 50 mm
[redacted]	[redacted] PIPE [redacted] 'B' TYPE) Ø 40 mm
[redacted]	[redacted] DOMESTIC WATER LINE Ø 40 mm
[redacted]	[redacted] DOMESTIC WATER LINE Ø 32 mm
[redacted]	[redacted] DOMESTIC WATER LINE Ø 25 mm
[redacted]	[redacted] DOMESTIC WATER LINE Ø 20 mm
[redacted]	[redacted] DOMESTIC WATER LINE Ø 15 mm
[redacted]	[redacted] WATER LINE Ø 15 mm
[redacted]	[redacted] HOT WATER LINE
[redacted]	[redacted] FLOOR [redacted]
[redacted]	[redacted]
[redacted]	[redacted]
[redacted]	[redacted] COCK
[redacted]	[redacted] VALVE
[redacted]	[redacted] VALVE
[redacted]	[redacted]
[redacted]	[redacted] WALL [redacted] WITH [redacted] TANK
[redacted]	[redacted]
[redacted]	[redacted]
[redacted]	[redacted] WALL
[redacted]	[redacted] SNK MAKE [redacted] DRAIN
[redacted]	[redacted] PIPE
[redacted]	[redacted] 450 X 450MM
[redacted]	[redacted] ARCH. PLAN
[redacted]	[redacted] ARCH. PLAN
[redacted]	[redacted] ARCH. PLAN
[redacted]	[redacted] ARCH. PLAN
[redacted]	[redacted]
[redacted]	[redacted]
[redacted]	DETAILS FLOOR PLAN
[redacted]	[redacted] & [redacted]
[redacted]	[redacted] AND [redacted] Colony, Vithalwadi Road, [redacted] 2432 0010
[redacted]	[redacted] LELE
[redacted]	[redacted]
NORTH	[redacted] 01.10.2019
	[redacted] G.
	[redacted] P.
SCALE:-NTS	[redacted] BY [redacted] P.

C:\Users\Dell\Downloads\ARC Plumbing Drawings (1)\ARC Plumbing Drawings\R5 Toilet Details 02.04.21.dwg

PRODUCED BY AN AUTODESK STUDENT VERSION

[redacted] BY AN [redacted] ENT VERSION