© [redacted] AND PARKER, P.C. 2014

SHEET KEY NOTES

1. EMERGENCY STORM DRAIN DISCHARGE TO GRADE PIPE 18"-24" ABOVE FINISHED GRADE. PROVIDE DISCHARGE NOZZLE WITH SCREEN. COORDINATE WITH CIVIL PLANS FOR GRADE ELEVATION.
2. PROVIDE ACCESS PANELS TO ALL DOMESTIC SUPPLY VALVES.
3. PROVIDE ACCESS PANELS TO ALL WATER HAMMER ARERESTORS. REFER TO PLUMBING RISER DIAGRAM FOR WATER HAMMER ARRESTOR LOCATION.

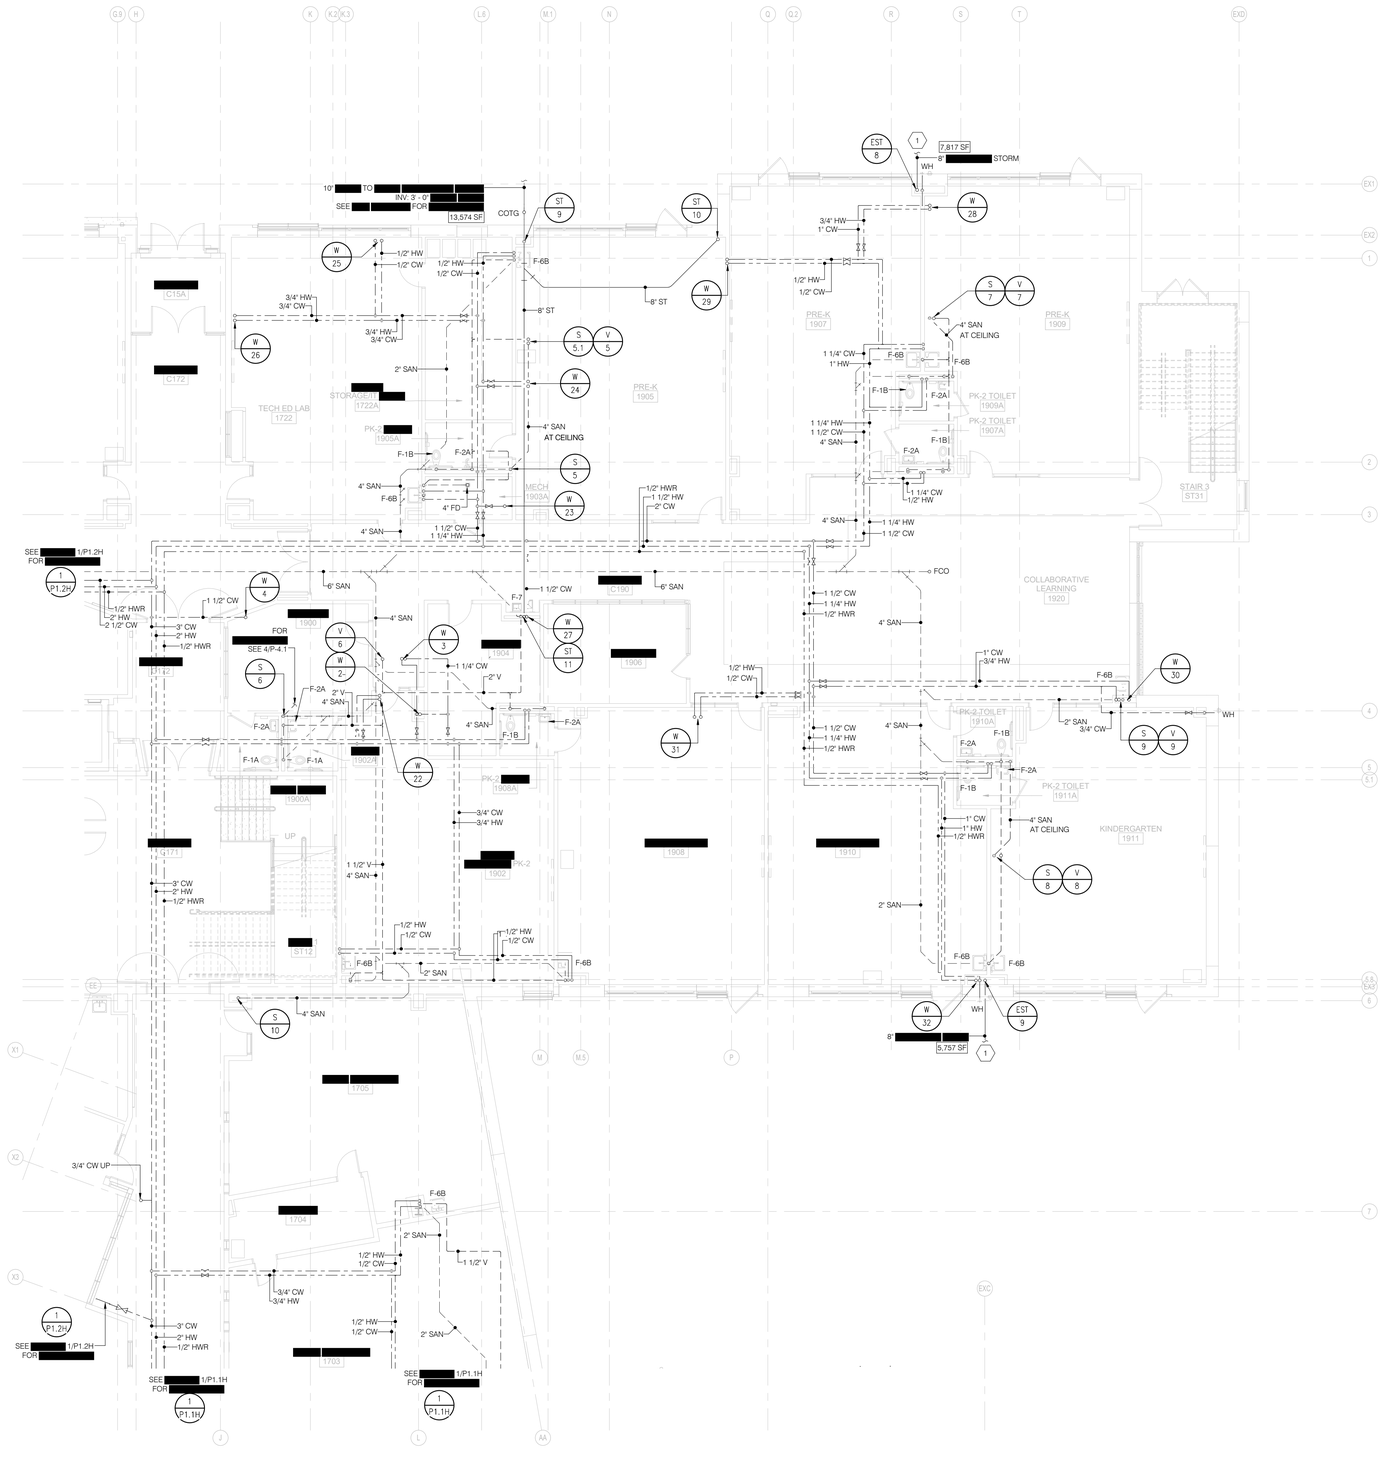

1 / P-1.3H FLOOR PLAN – AREA C

SCALE: 1/8" = 1'-0"

KEY PLAN

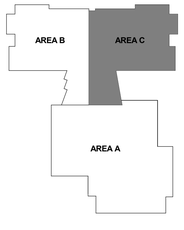

SETTY
ONE SOUTH STREET, SUITE 1130
BALTIMORE, MARYLAND 21202
TEL 667-329-5035
WASHINGTON | BALTIMORE | HARRISBURG | PITTSBURGH
ENERGY MANAGEMENT SERVICES • DESIGN BUILD SERVICES
CONSULTING ENGINEERS • CONSTRUCTION MANAGEMENT
DISTRICT OF COLUMBIA | MARYLAND
www.SETTY.com
PROJECT NUMBER 2016-0117.0 0 0 0 0

11720 Beltsville Drive
Suite 600
Calverton, MD 20705
Tel: 301.595.1000
www.grimmandparker.com
G+P GRIMM AND PARKER

GP# 21553

PLUMBING PARTIAL FIRST FLOOR PLAN – AREA C

HOLABIRD ACADEMY PK-8
CITY OF BALTIMORE, MARYLAND

DATE	DESCRIPTION

P-1.3H

03/13/2017
BID SET

© GRIMM AND PARKER, P.C. 2014