GENERAL BASEMENT NOTES:

1. 1" WATER LINE REQUIRED TO ALL WATER HEATERS.
2. WATER HEATERS TO HAVE ENGINEERED SEISMIC CONNECTION STRAPS.
3. COMBUSTION AIR MUST ENTER FROM EXTERIOR OF MECHANICAL ROOM.
4. ALL CONCRETE BELOW FINAL GRADE MUST HAVE DAMP PROOFING.
5. 1 EGRESS LANDER REQUIRED IF NO OTHER EXIT.

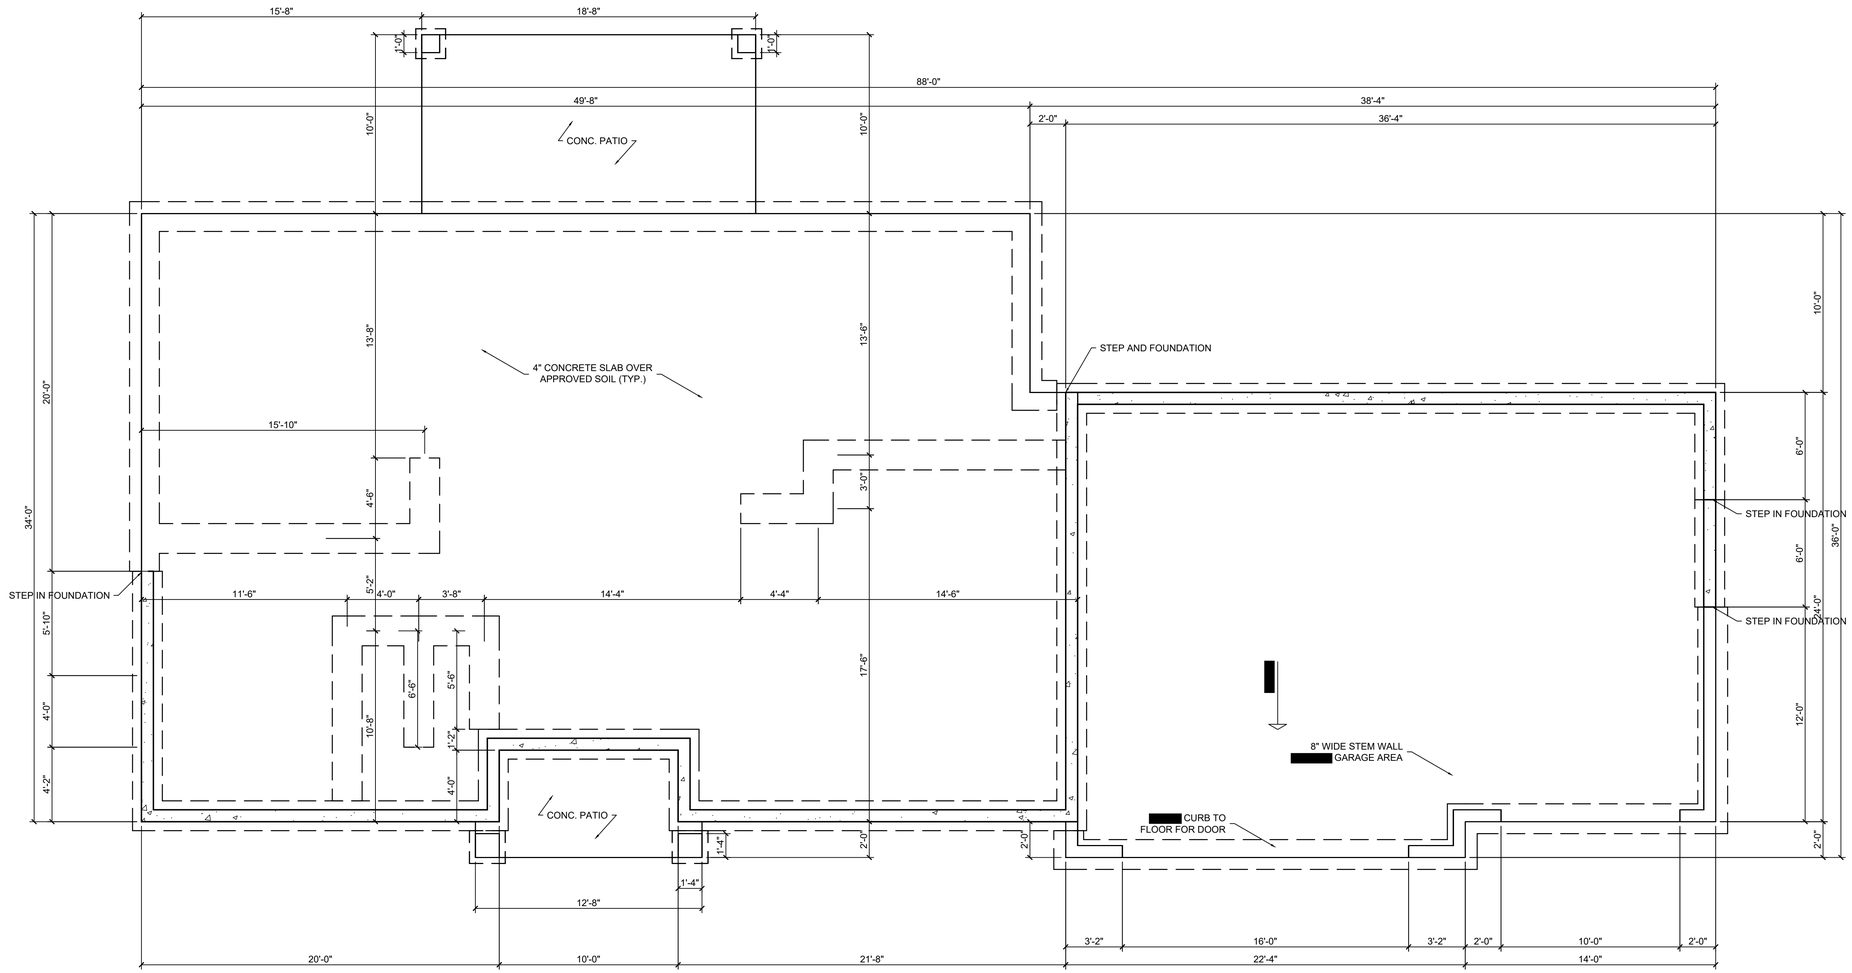

FTG & FOUNDATION PLAN

SCALE: ¼" = 1'-0"

[redacted]
[redacted] #
20-142
REV.1
-
REV.2
-
[redacted] REV.
1/11/2021

[redacted]
305 W. Shangri-La
Toquerville, UT 84774

FTG & FOUNDATION PLAN

J. LONNIE FOX
DRAFTING AND DESIGN
phone (801)-871-1442 • jlonniefox@gmail.com • www.jlfdraftingdesign.com

[redacted] SQFT	1713
MAIN FLR SQFT	1705
2ND FLR SQFT	0
GARAGE SQFT	909
[redacted] FIN SQFT	3418
[redacted] SQFT	3418

[redacted] #
A1.1

2020 J. FOX AND DESIGN, THE IS A USE FOR ONLY. ARE AND ARE TO AS AN WORK" THE ACT: