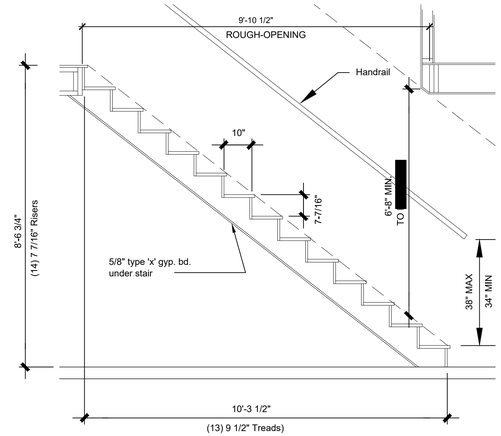

TYP. STAIR DETAIL

SCALE: NTS

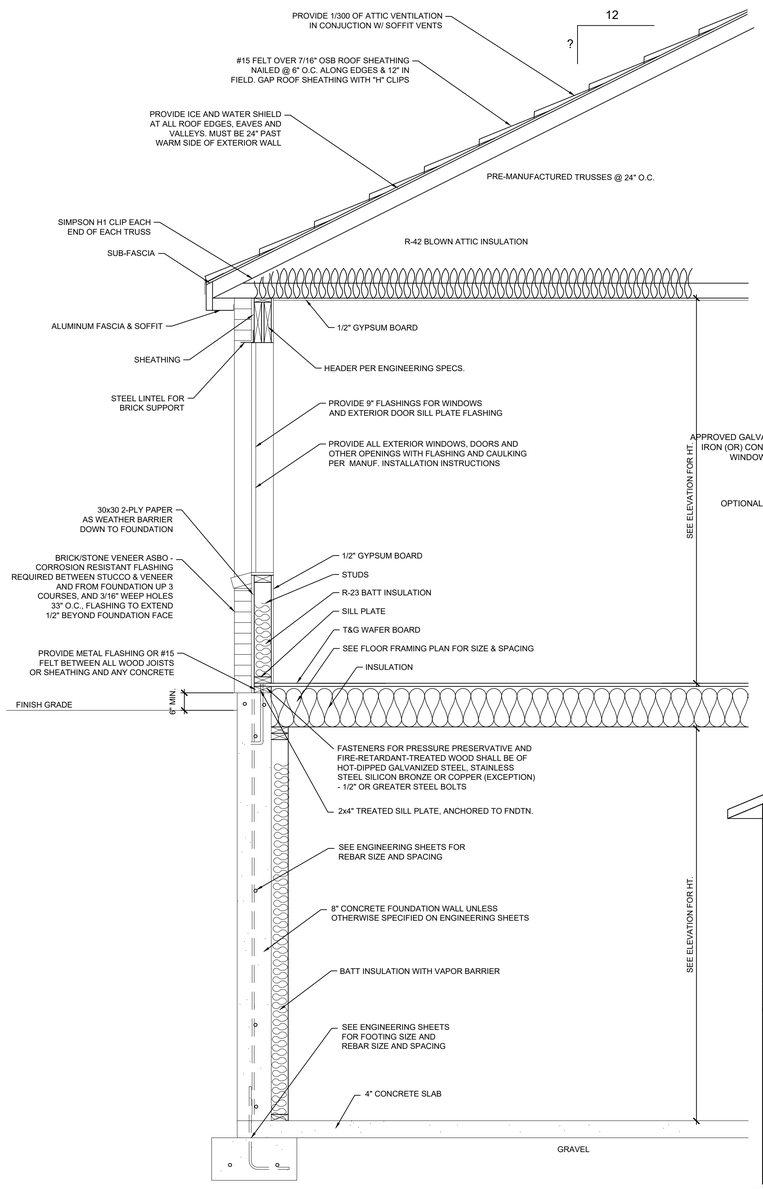

TYP. WALL SECTION DETAIL

SCALE: ¾" = 1'-0"

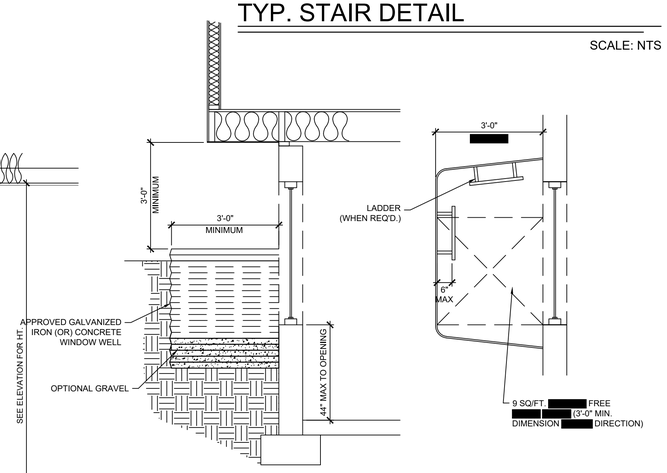

TYP. WINDOW WELL DETAIL

SCALE: NTS

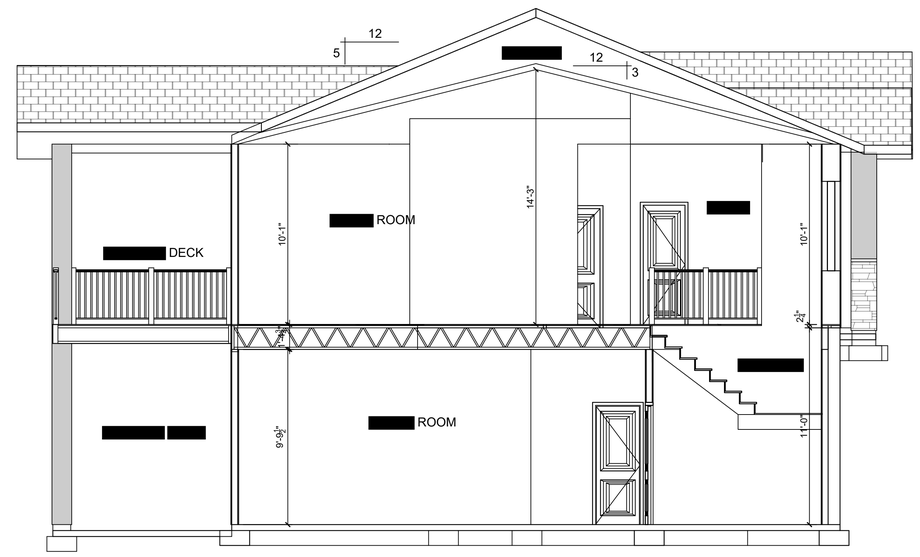

1 SECTION

SCALE: ¼" = 1'-0"

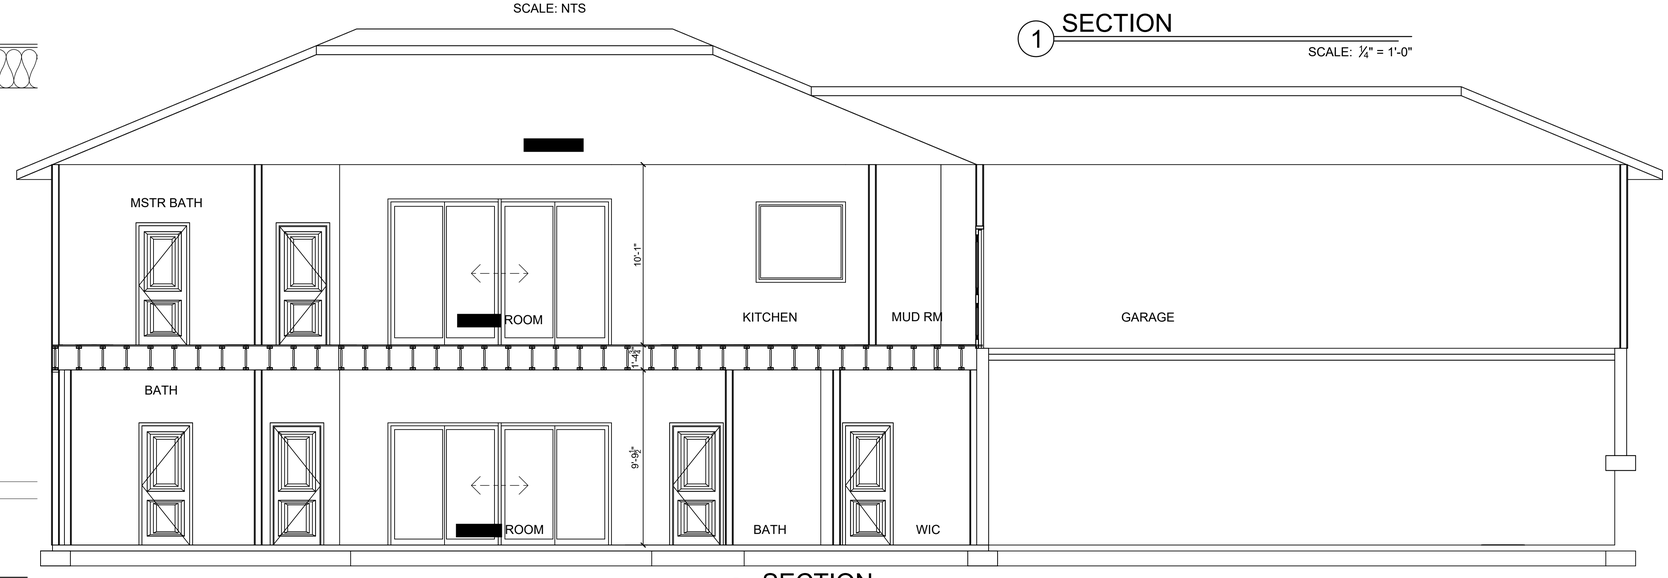

2 SECTION

SCALE: ¼" = 1'-0"

[redacted] Y
[redacted] #
20-142
REV.1
-
REV.2
-
[redacted] REV.
1/11/2021

[redacted]

[redacted]
305 W. Shangri-La
Toquerville, UT 84774

[redacted]

J. LONNIE FOX
DRAFTING AND DESIGN
phone: (801) 987-1442 • jlonniefox@gmail.com • www.jlfdraftingdesign.com

[redacted] SQFT	1713
MAIN FLR SQFT	1705
2ND FLR SQFT	0
GARAGE SQFT	909
[redacted] FIN SQFT	3418
[redacted] SQFT	3418

[redacted] #
A3.1

2020 J. FOX AND DESIGN. THE [redacted] IS A USE FOR ONLY [redacted] ARE AND ARE TO [redacted] AS AN [redacted] WORK" [redacted] THE [redacted] ACT.